



Mountain Prairie Acres: Whole-Site Terrain and Water

The whole 10-acre lot to scale, north up, as it lies today: elevation and contours, where water goes, and slope. Base maps for planning future projects anywhere on the property.


1 · Elevation and contours

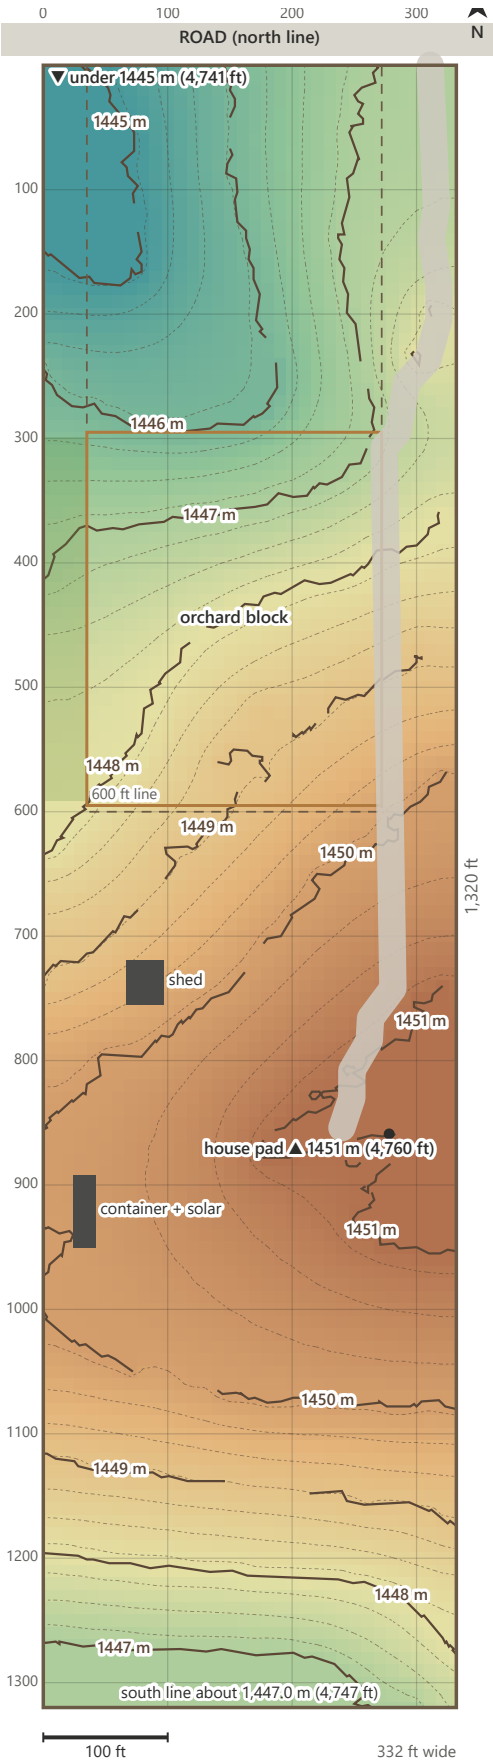

2 · Where water goes

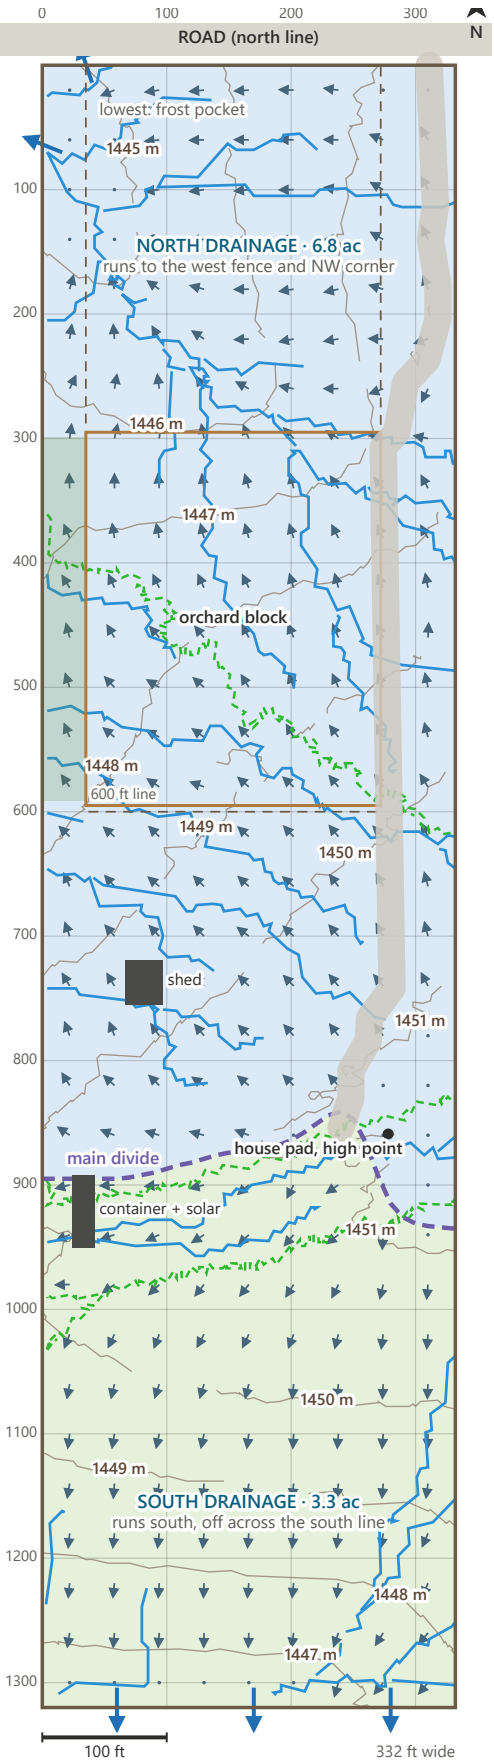


3 · Slope and planning

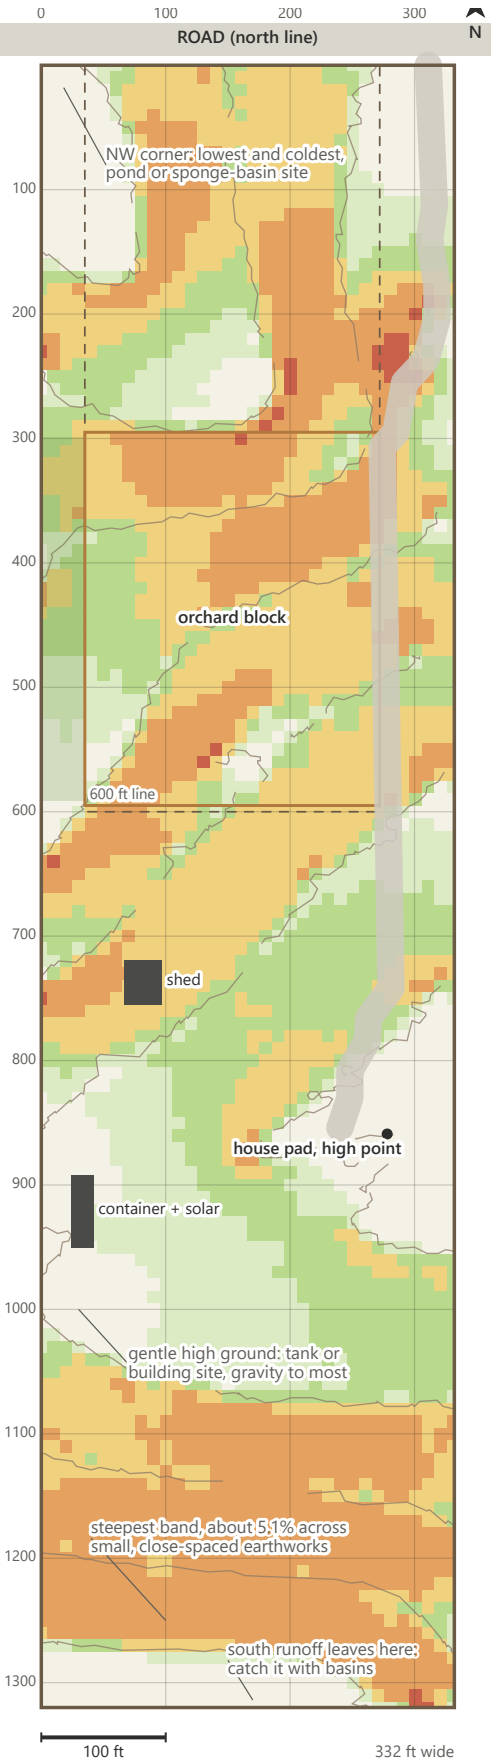

LOT 10.1 acres 332 × 1,320 ft, fence to fence	HIGHEST 1451 m about 4,760 ft, the homestead pad
LOWEST under 1445 m about 4,741 ft, NW corner by the road	RELIEF about 20 ft from the pad down to the NW corner
NORTH DRAINAGE 6.8 acres to the west fence and NW corner	SOUTH DRAINAGE 3.3 acres south, across the south line
TYPICAL SLOPE 3.1% most ground 0.6%–4.7%	SOIL Simonton loam loam over clay loam; deep, well drained

Legend

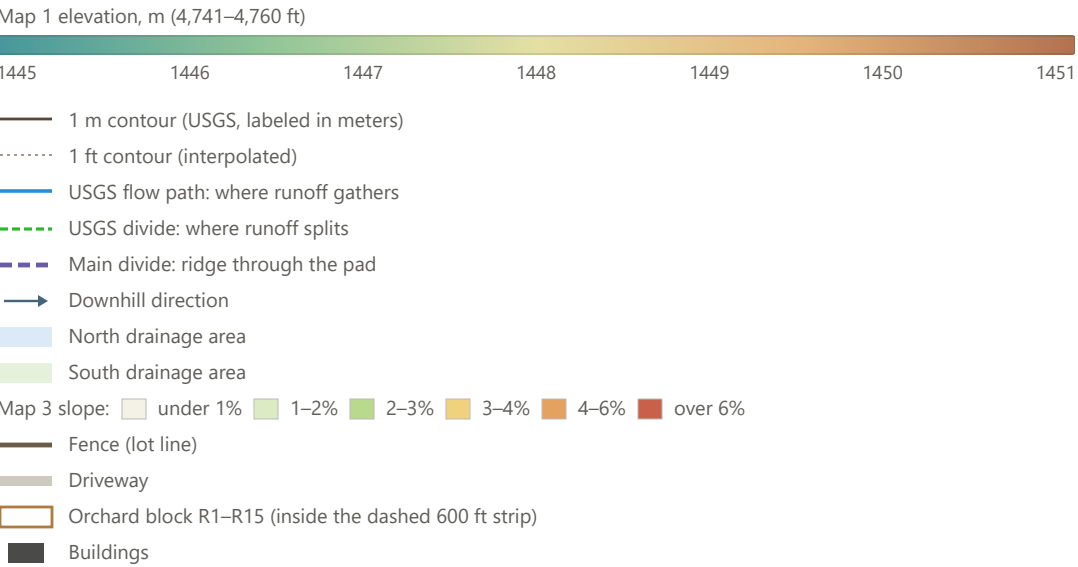


For future projects

- High ground: the homestead pad (about 1451 m) tops both drainages. A tank there sits about 20 ft above the NW corner, roughly 9 psi by gravity at the lowest point and less closer in.
- North drainage (6.8 acres): everything north of the main divide runs north and west to the west fence and the NW corner. The corner is the lowest, wettest, and coldest spot: a place for a pond, sponge basin, or wet-tolerant plants, not frost-tender ones.
- South drainage (3.3 acres): south of the divide, runoff leaves the lot across the south line. Basins or swales there keep that water on your ground for future plantings.
- Blue flow paths mark where runoff gathers. Keep buildings, driveways, and tanks out of them; use them for swales, basins, or a pond.
- Slope: most of the lot is gentle (typical 3.1%). Flatter ground suits buildings, gardens, and level basins; on the steeper bands, use smaller, closer-spaced earthworks and keep the ground covered.
- Cold air drains like water, so frost settles first in the NW corner and along the low west side.
- To place a project, read its coordinates off the 100 ft grid, then its elevation from map 1 or the spot table on page 2. Check with a level before building.

All three maps share one scale, north up. Coordinates are feet east of the west fence and feet south of the north line (the road); grid lines are 100 ft apart. Traced from USGS 1 m maps; elevations between contours are interpolated, good to about a foot.

Profiles, Spot Elevations, and Key Points

North–south profiles, road to south line

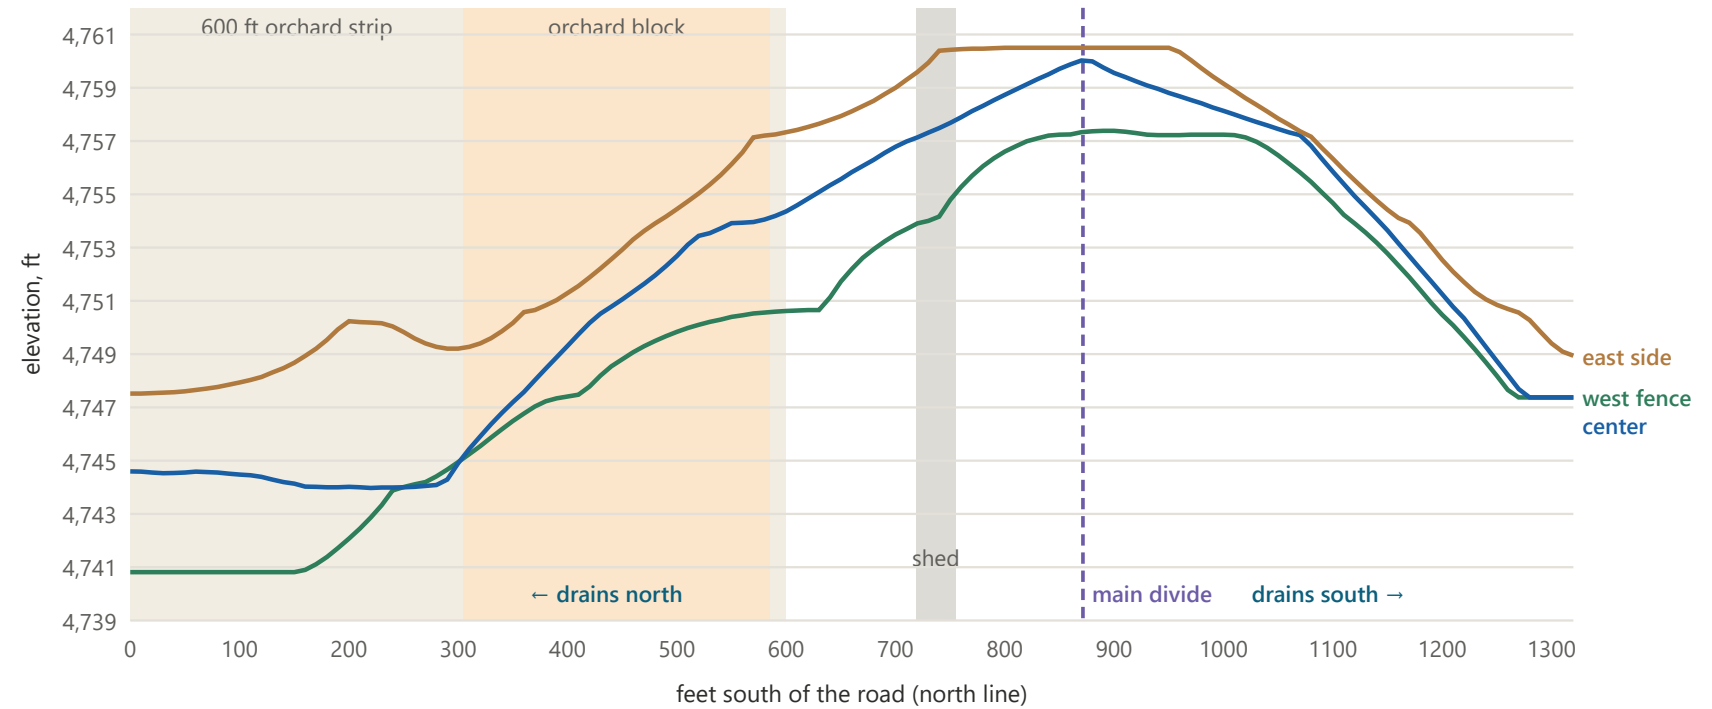


Spot elevations in feet, every 100 ft south of the road

South ↓ / east →	0	50	100	150	200	250	300	332
0	4,741	4,741	4,742	4,744	4,746	4,747	4,747	4,748
100	4,741	4,741	4,742	4,744	4,746	4,747	4,748	4,748
200	4,742	4,742	4,743	4,744	4,745	4,747	4,750	4,750
300	4,745	4,745	4,744	4,745	4,746	4,747	4,749	4,749
400	4,747	4,748	4,748	4,749	4,750	4,750	4,751	4,751
500	4,750	4,750	4,751	4,752	4,753	4,754	4,754	4,754
600	4,751	4,751	4,753	4,754	4,755	4,756	4,757	4,757
700	4,753	4,754	4,755	4,756	4,757	4,758	4,759	4,759
800	4,757	4,757	4,758	4,758	4,759	4,760	4,760	4,760
900	4,757	4,758	4,758	4,759	4,760	4,760	4,760	4,760
1,000	4,757	4,757	4,758	4,758	4,758	4,759	4,759	4,759
1,100	4,755	4,755	4,755	4,756	4,756	4,756	4,756	4,756
1,200	4,750	4,751	4,751	4,751	4,751	4,752	4,752	4,753
1,300	4,747	4,747	4,747	4,747	4,747	4,747	4,749	4,750
1,320	4,747	4,747	4,747	4,747	4,747	4,747	4,747	4,749

Columns are feet east of the west fence. Shading follows the elevation colors on map 1. One meter is 3.28 ft.

East–west cross-sections (vertical scale exaggerated)

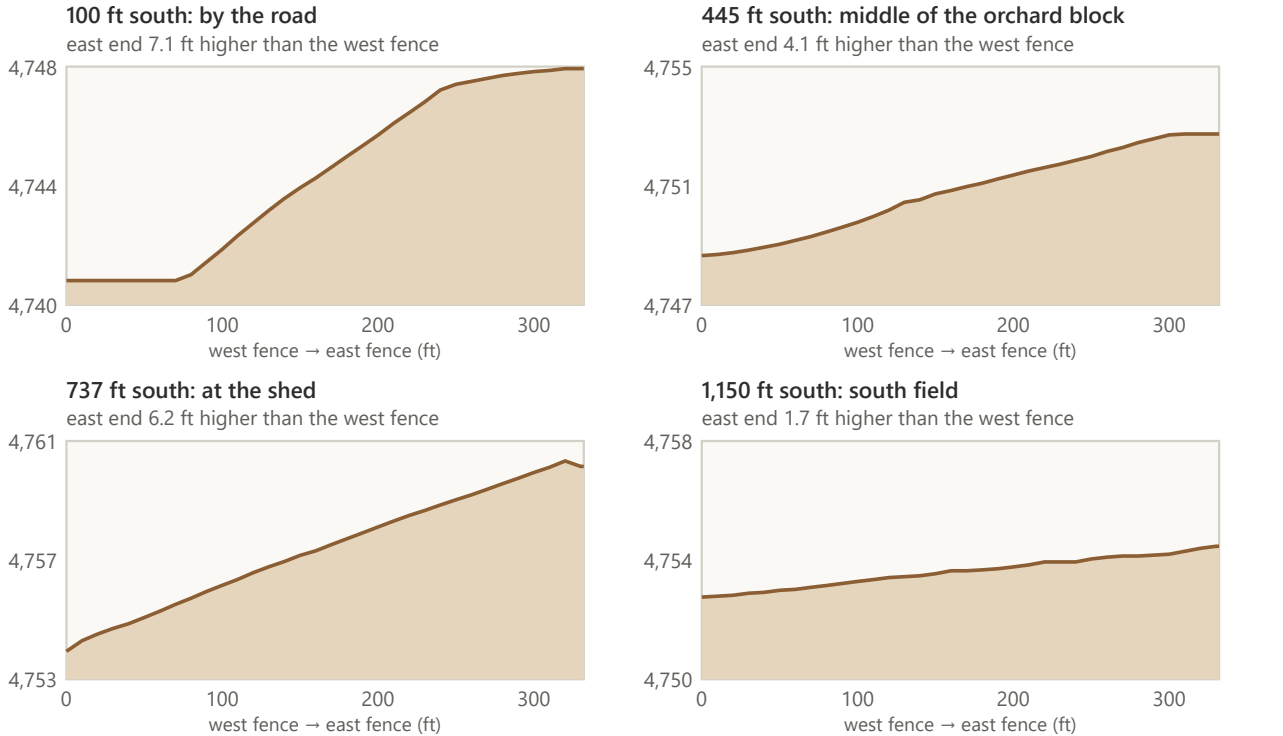

Key points

Point	x, y (ft)	m	ft	Above NW corner
NW corner, lowest	0, 0	1,445.0	4,741	0.0 ft
NE corner	332, 0	1,447.0	4,748	6.7 ft
R15 row, center	154, 305	1,446.3	4,745	4.2 ft
R1 row, center	154, 585	1,449.0	4,754	13.1 ft
Shed	82, 737	1,449.6	4,756	15.0 ft
House pad, high point	278, 859	1,451.0	4,760	19.7 ft
Main divide, center	166, 871	1,450.9	4,760	19.2 ft
SW corner	0, 1,320	1,447.0	4,747	6.6 ft
SE corner	332, 1,320	1,447.5	4,749	8.3 ft

How these maps were made

- Contours (1 m interval), flow paths, and divides traced from the owner's USGS 1 m elevation maps (October 6, 2026), scaled to the fences: 332 ft fence to fence, 1,320 ft from the north line to the south line.
- Elevation between contours interpolated on a 5 ft grid (smooth surface through the contour lines), sampled every 10 ft. 1 ft contours, slope, flow arrows, profiles, and the main divide come from that surface.
- Driveway traced from the USGS aerial; shed and container from their roofs; the house pad is the high ground inside the 1451 m contour. Orchard layout from the pollination grid (October 4, 2026), with R1 about 15 ft inside the south end of the 600 ft strip.
- Soil: USDA NRCS Web Soil Survey report for the property, map unit 149, Simonton loam, 2 to 12 percent slopes.