


Mountain Prairie Acres: Homestead Plot Map

The homestead to scale, north up, as it stood in October 2026: buildings, containers, tank, pump house, pads, the road-mix drives, and the buried water lines and hydrants, on the 50 ft master grid. Planned buildings are dashed.

Homestead, 50 ft grid cells (see the Site Master Grid)

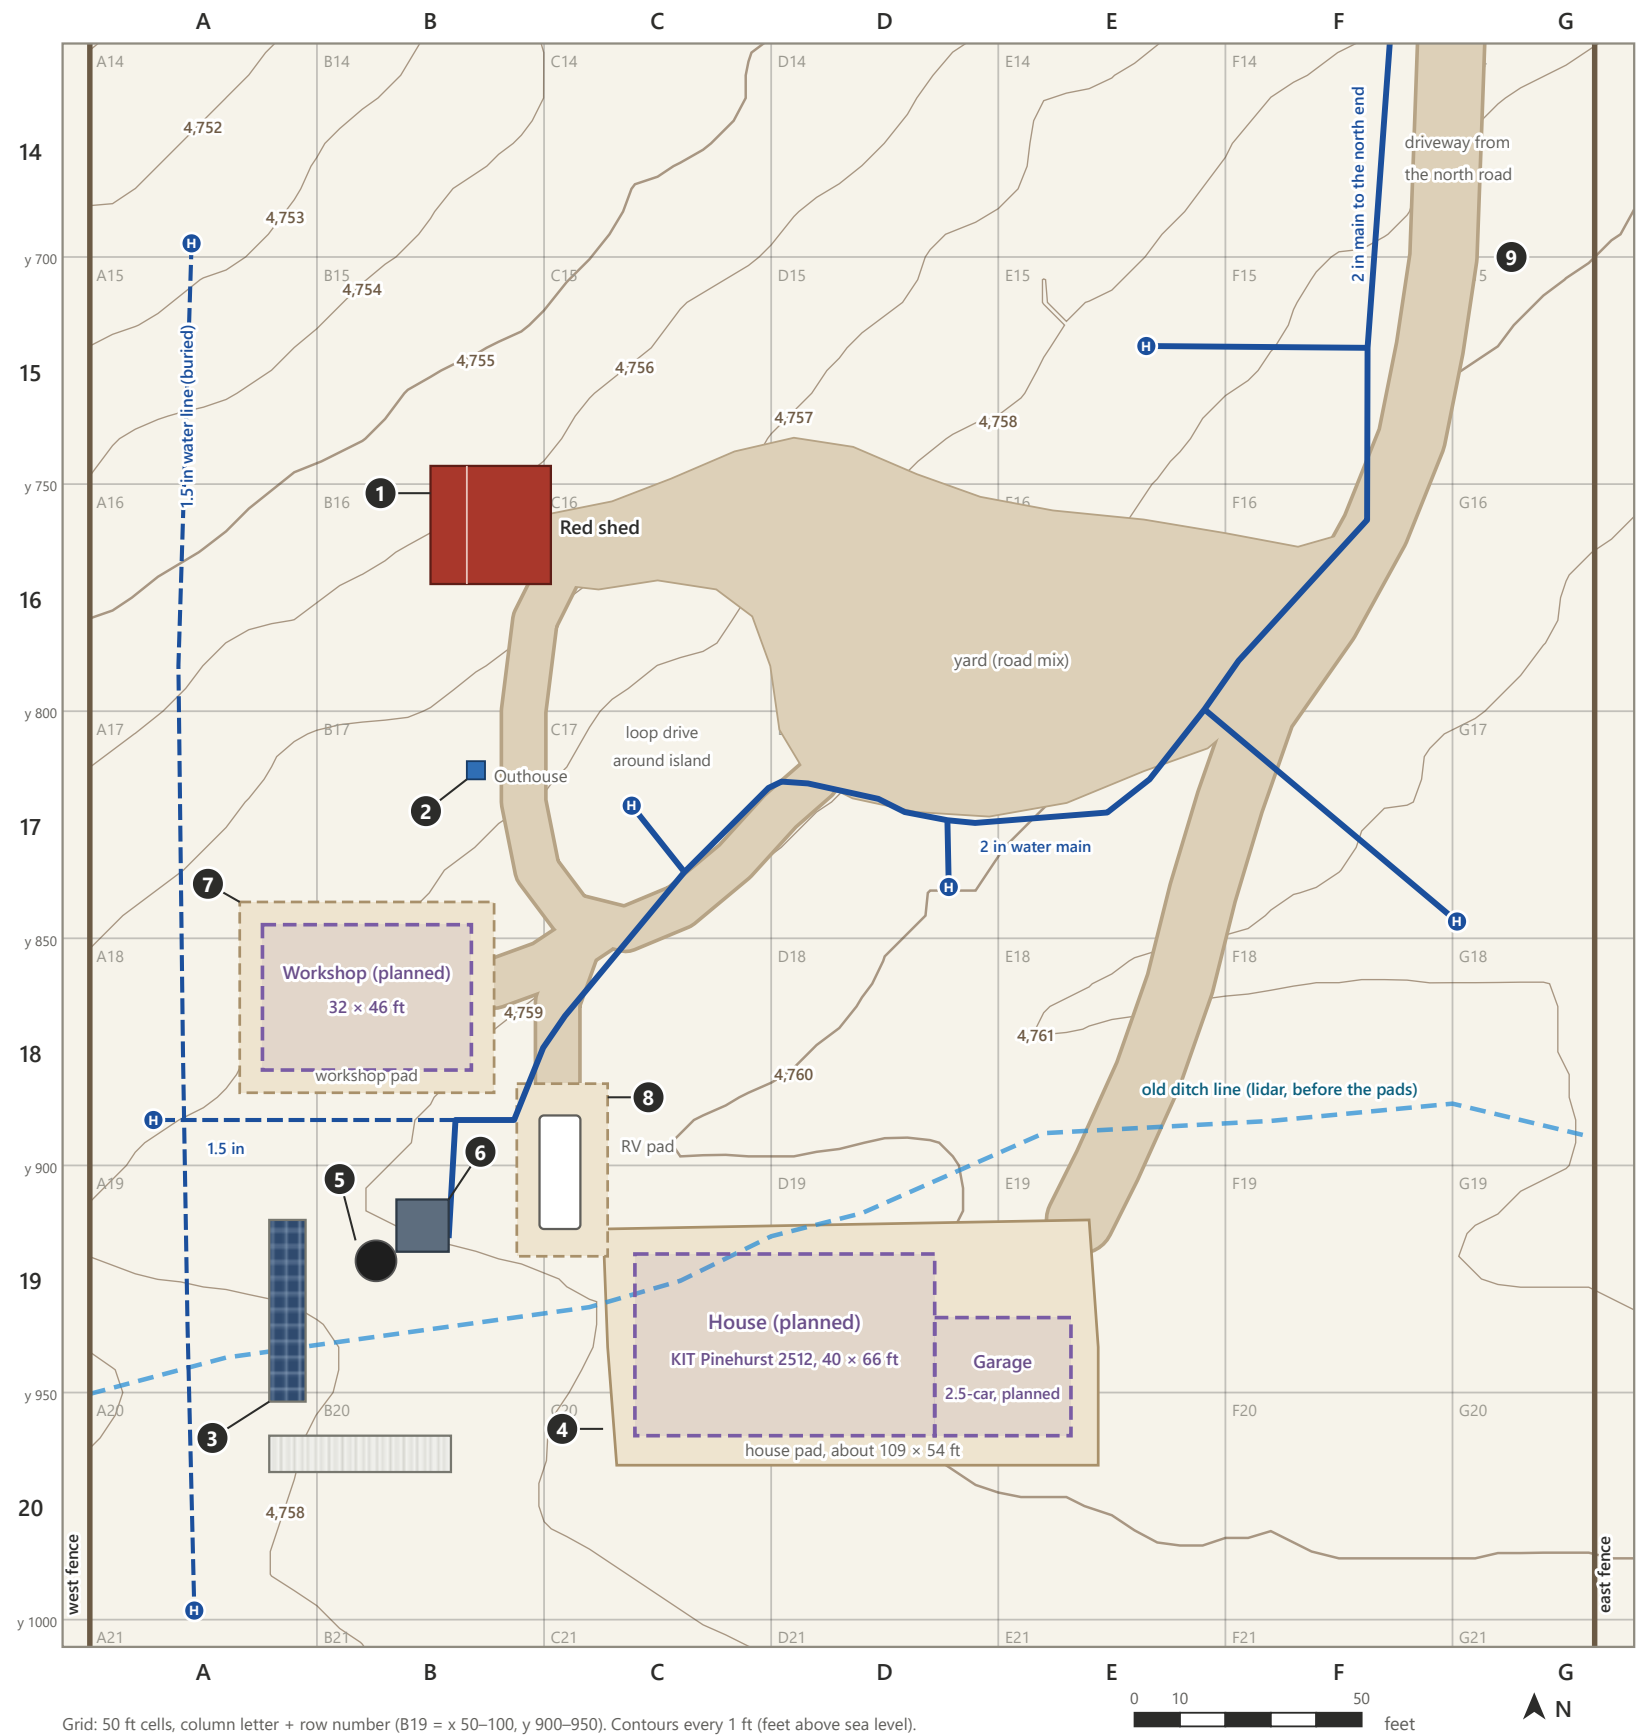

Legend

- Red shed (with west lean-to)

Storage container

RV camper

Road mix: drives and paths

Water main and branches, 2 in PVC

1 ft contour, ground before the pads
- Outhouse

Irrigation tank, 3,500 gal

Planned building

Fence (lot line)

Water line, 1.5 in PVC

Item number (inventory)
- Solar container

Pump house

Graded pad

Old ditch line (lidar)

Frost-free yard hydrant

Inventory (numbers match the map)

#	Item	Size, ft	Cell	Center x, y	Ground, ft
1	Red shed	26.5 × 26	B16	88, 759	4,756.2
2	Outhouse	4 × 4	B17	85, 813	4,757.7
3	Solar container	8 × 40	A19	44, 932	4,757.9
3	Storage container	40 × 8	B20	60, 964	4,758.3
4	House pad	109 × 54	D19	168, 939	4,759.8
4	House (planned)	66 × 40	D19	153, 940	4,759.6
4	Garage (planned)	30 × 26	E19	201, 947	4,760.2
5	Irrigation tank	9 across	B19	63, 921	4,758.7
6	Pump house	11.5 × 11.5	B19	73, 913	4,759.1
7	Workshop pad	56 × 42	B18	61, 863	4,758.4
7	Workshop (planned)	46 × 32	B18	61, 863	4,758.4
8	RV pad	20 × 38	C19	104, 901	4,759.5
8	RV camper	9 × 25	C19	104, 902	4,759.5
9	Driveway (north road to the pad)	14 wide, 950 long	G1 → E19	—	—
9	Yard and turnaround	8,400 sq ft	D16	193, 780	4,759.0
9	Loop drive around the island	9 wide, 150 long	C16 → D17	102, 839	4,758.4
	Water main, 2 in PVC	2 in pipe, 1,015 long	B19 → G1	—	—
H	Frost-free yard hydrants (8)	—	F1, A14, E15, C17, D17, G17, A18, A20	—	—

Gaps for pipe, wire, and path runs (edge to edge)

From → to	Gap, ft	Ground at the far end
Pump house → house (planned)	41	0.3 ft higher
Pump house → garage (planned)	108	1.1 ft higher
Pump house → workshop (planned)	29	0.3 ft lower
Pump house → RV	20	0.2 ft higher
Pump house → shed	136	2.7 ft lower
Tank → orchard block (R1 row)	322	7.6 ft lower
House pad → low point (NW corner)	869	20.3 ft lower

Notes

- Placed from the owner's drone photos (October 2026), fitted to USGS aerial imagery and lidar: buildings, containers, tank, and pump house to about 3 ft; pad edges and paths to 5–10 ft.
- Planned house (40 × 66), garage (east end, flush with the house's south wall, about 30 × 26 placeholder), and workshop (32 × 46, long side east–west) are drawn where the owner described them; move them in data/site_grid.js once their final spots are staked.
- Old ditch: the lidar, flown before the pads were graded, shows a shallow ditch with a berm on its north side running west along the north edge of the house pad and past the containers. If any of it remains, grade so runoff passes around the house, containers, and pump house, not against them.
- Water lines and hydrants are traced from the owner's hand-drawn map (October 2026), to about 5 ft; the 1.5 in line along the west fence is the covered trench in the drone photo. Keep posts, tree holes, and other digging off them.
- The homestead sits near the top of the lot: the house pad is about 1–2 ft below the highest ground (east fence) and roughly 20 ft above the NW corner, so water lines to the orchard run downhill.

Coordinates are feet east of the west fence (x) and feet south of the north fence (y); the driveway entrance on the north road is at 43.47550, -115.59364. Ground elevations are from USGS lidar flown before the pads were graded.